DOSSIER DE MUTATION No : 1/2023

Commune : **Satigny**

Section :

Provisoire à l'examen

Plan : 72
Immeuble : 7177
Bâtiment : Projeté
Situation : Route d'Aire-la-Ville 147-149-149A

PROPRIÉTÉ PAR ÉTAGES

Constituée avant la construction

Cahier de répartition des locaux

Dont la conformité aux prescriptions de l'art. 712b al. 1 CCS est certifiée par l'Ingénieur géomètre officiel soussigné

Repose sur fonds voisin ○ oui ◉ non

Pièces du dossier :

1. Titre	(1)
2. Plan de situation	(1)
3. Elévation	(1)
4. Plans de répartition des locaux	(6)
5. Tableau de répartition des locaux et calcul des éléments constitutifs	(3)
6. Tableau récapitulatif	(3)
7. Servitude(s)	(4)

L'auteur du dossier :

KÜPFER GÉOMÈTRES SA
INGÉNIEUR GÉOMÈTRE OFFICIEL EPF/AGG
RUE EUGÈNE-MARZIANO 41
CH 1227 LES ACACIAS
TEL 022 732 03 12
kupfer-geometre.ch
akupfer@worldcom.ch
Ingénieurs géomètres brevetés Küpfer Adrien - Aure Rachel

IGO : Adrien Küpfer
Dossier n° 2794
Etabli le : 03.03.2023 /GDC
Dernière modification le: 22.11.2023
Vérifié le:

Acte dressé par
Maître :
Réf. .....

DIT
Direction de l'Information du Territoire

Déposé le .....
.....
Introduction en base de données
effectuée le .....

Plan de situation

KÜPFER GÉOMÈTRES SA
INGÉNIEUR GÉOMÈTRE OFFICIEL EPF/AGG
RUE EUGÈNE-MARZIANO 41
CH 1227 LES ACACIAS
TEL 022 732 03 12
kupfer-geometre.ch
akupfer@worldcom.ch

Commune	:	Satigny
Section	:	–
Plan No	:	72
Echelle	:	1:500
Date	:	03.03.2023
Dernière modif.	:	22.11.2023

Dossier : 2794 / GDC

	Numéro	Surface	Destination	Observations
Parcelle	7177	5017m²		
Bâtiment	Projet	-	Hab. plusieurs logements	
Bâtiment	Projet	-	Hab. plusieurs logements	
Bâtiment	Projet	-	Garage (sous-sol)	

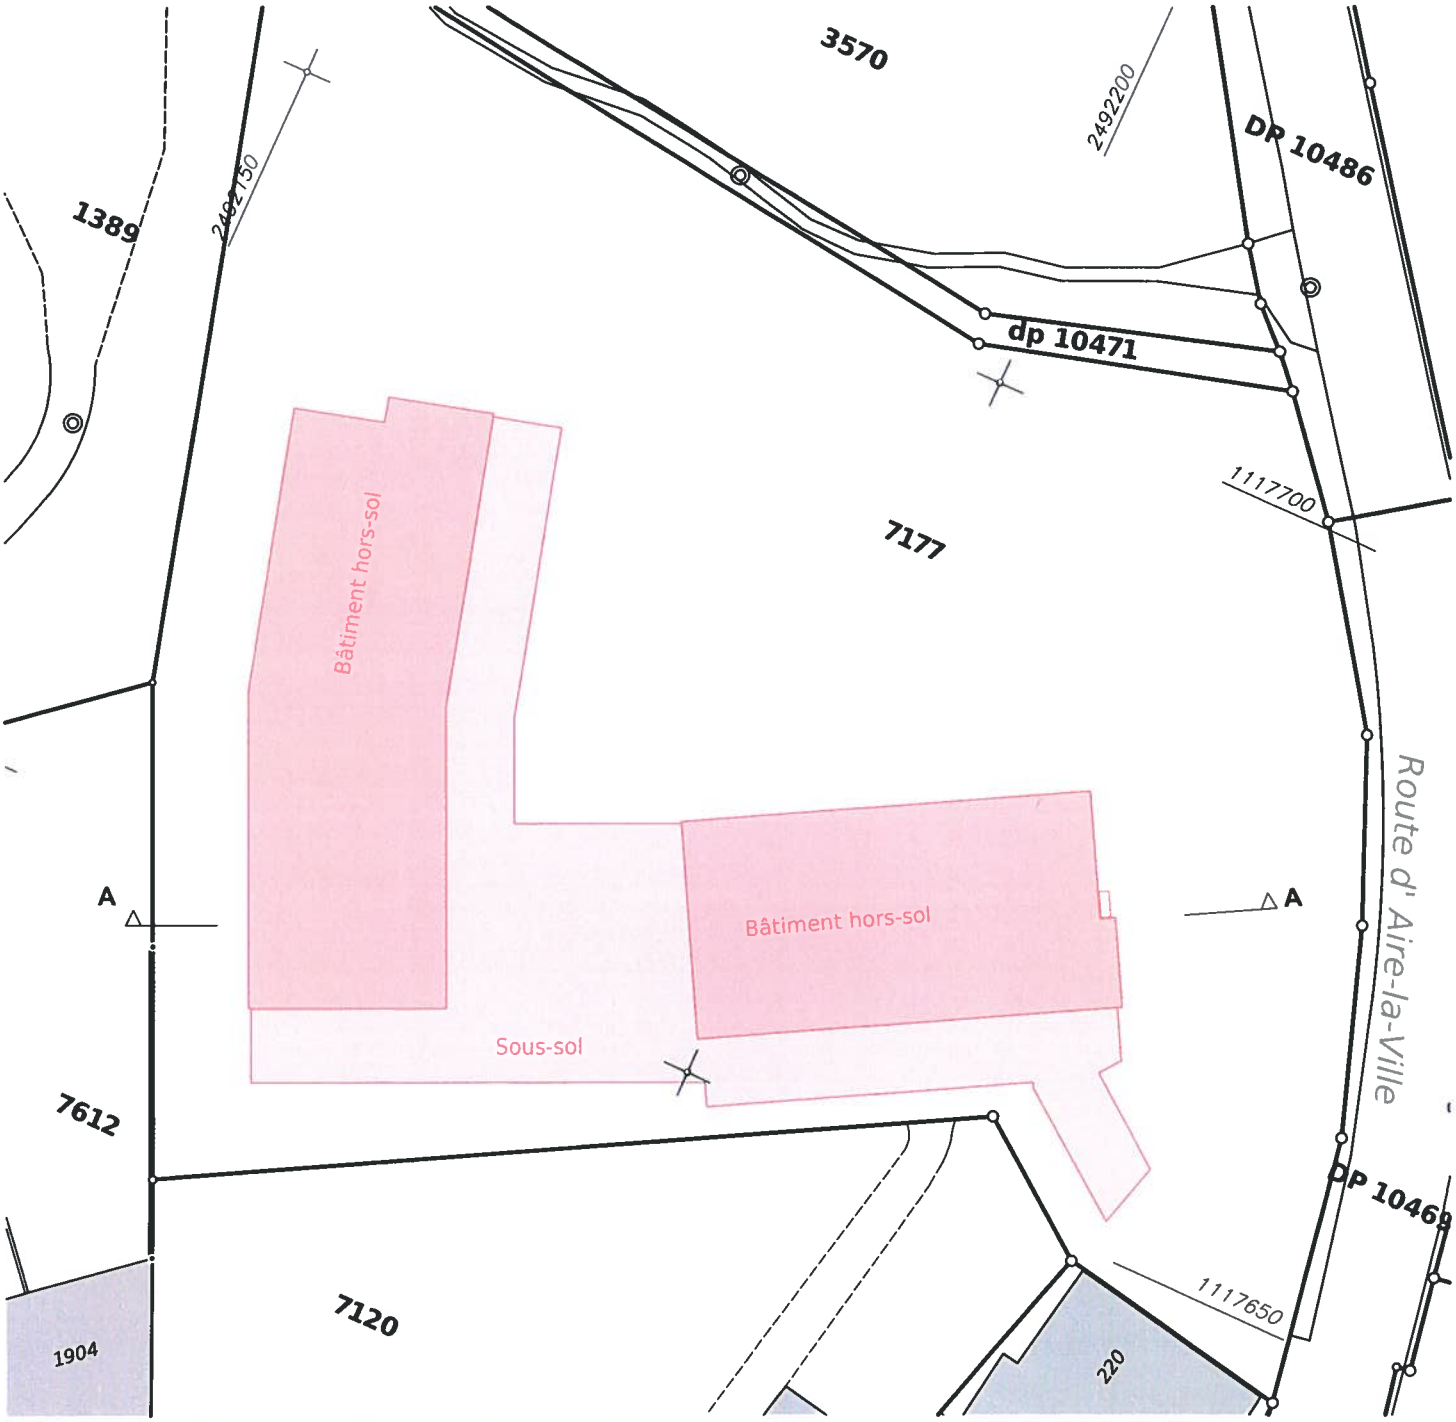

Elevation - Coupe AA

KÜPFER GÉOMÈTRES SA
INGÉNIEUR GÉOMÈTRE OFFICIEL EPF/AGG
RUE EUGÈNE-MARZIANO 41
CH 1227 LES ACACIAS
TEL 022 732 03 12
kupfer-geometre.ch
akupfer@worldcom.ch

Dossier : 2794 / GDC

Commune	:	Satigny
Section	:	–
Plan No	:	72
Date	:	03.03.2023
Dernière modif.	:	-

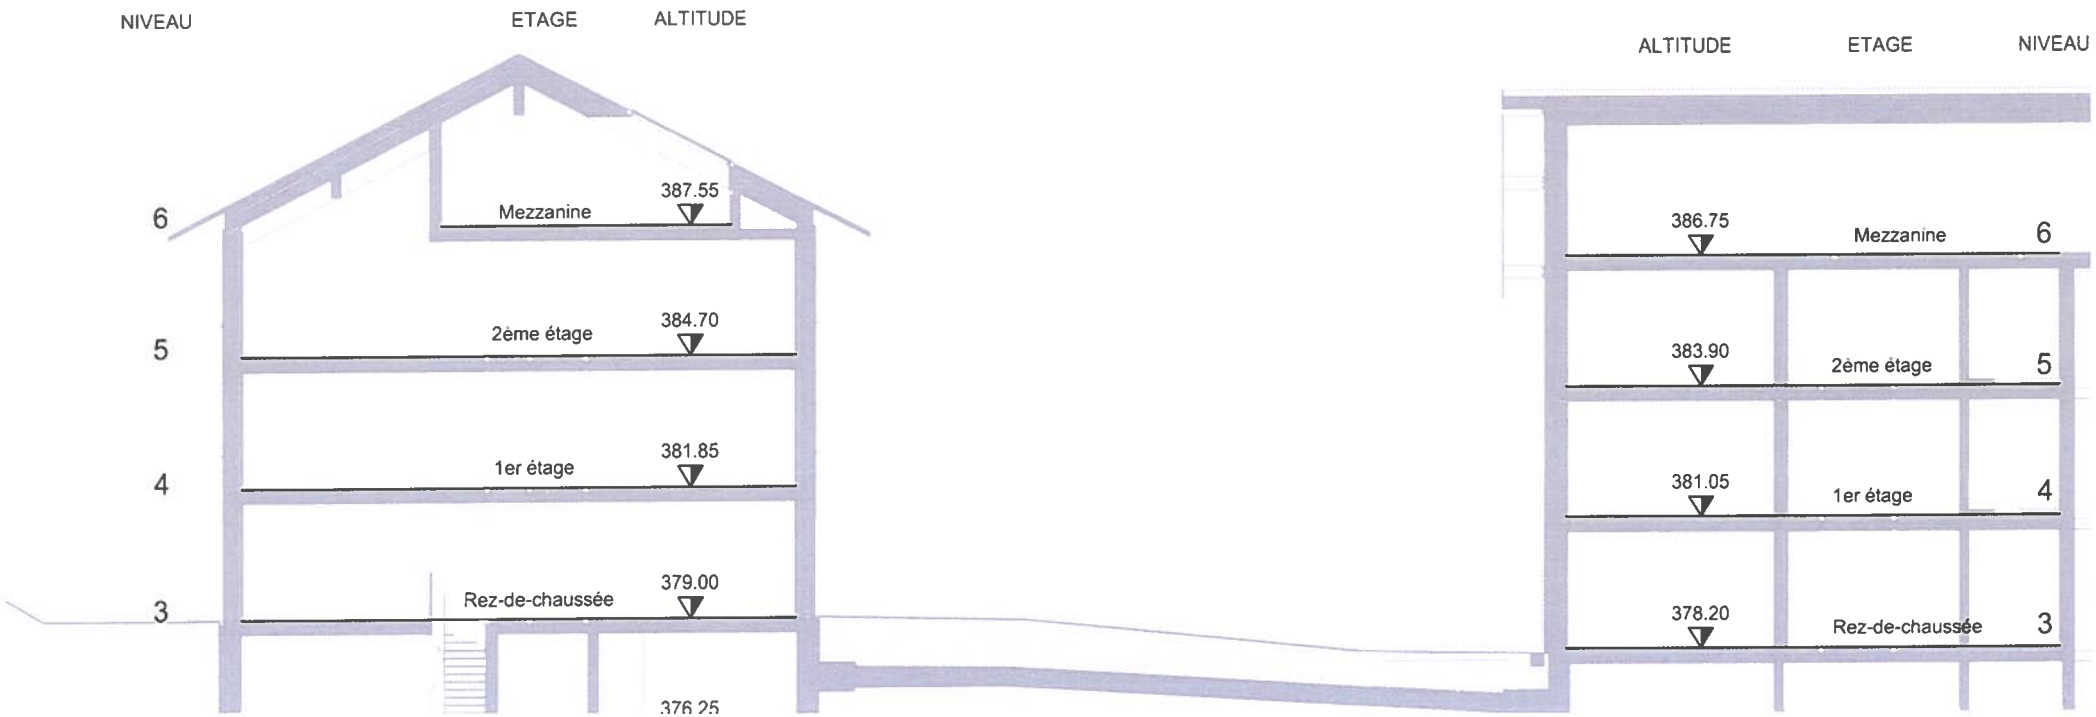

Plan de répartition des locaux

KÜPFER GÉOMÈTRES SA
INGÉNIEUR GÉOMÈTRE OFFICIEL EPF/AGG
RUE EUGÈNE-MARZIANO 41
CH 1227 LES ACACIAS
TEL 022 732 03 12
kupfer-geometre.ch
akupfer@worldcom.ch

Dossier : 2794 / GDC

Bâtiment	:	Projet
Niveau (sous-sol)	:	1
Echelle	:	1:500
Date	:	03.03.2023
Dernière modif.	:	-

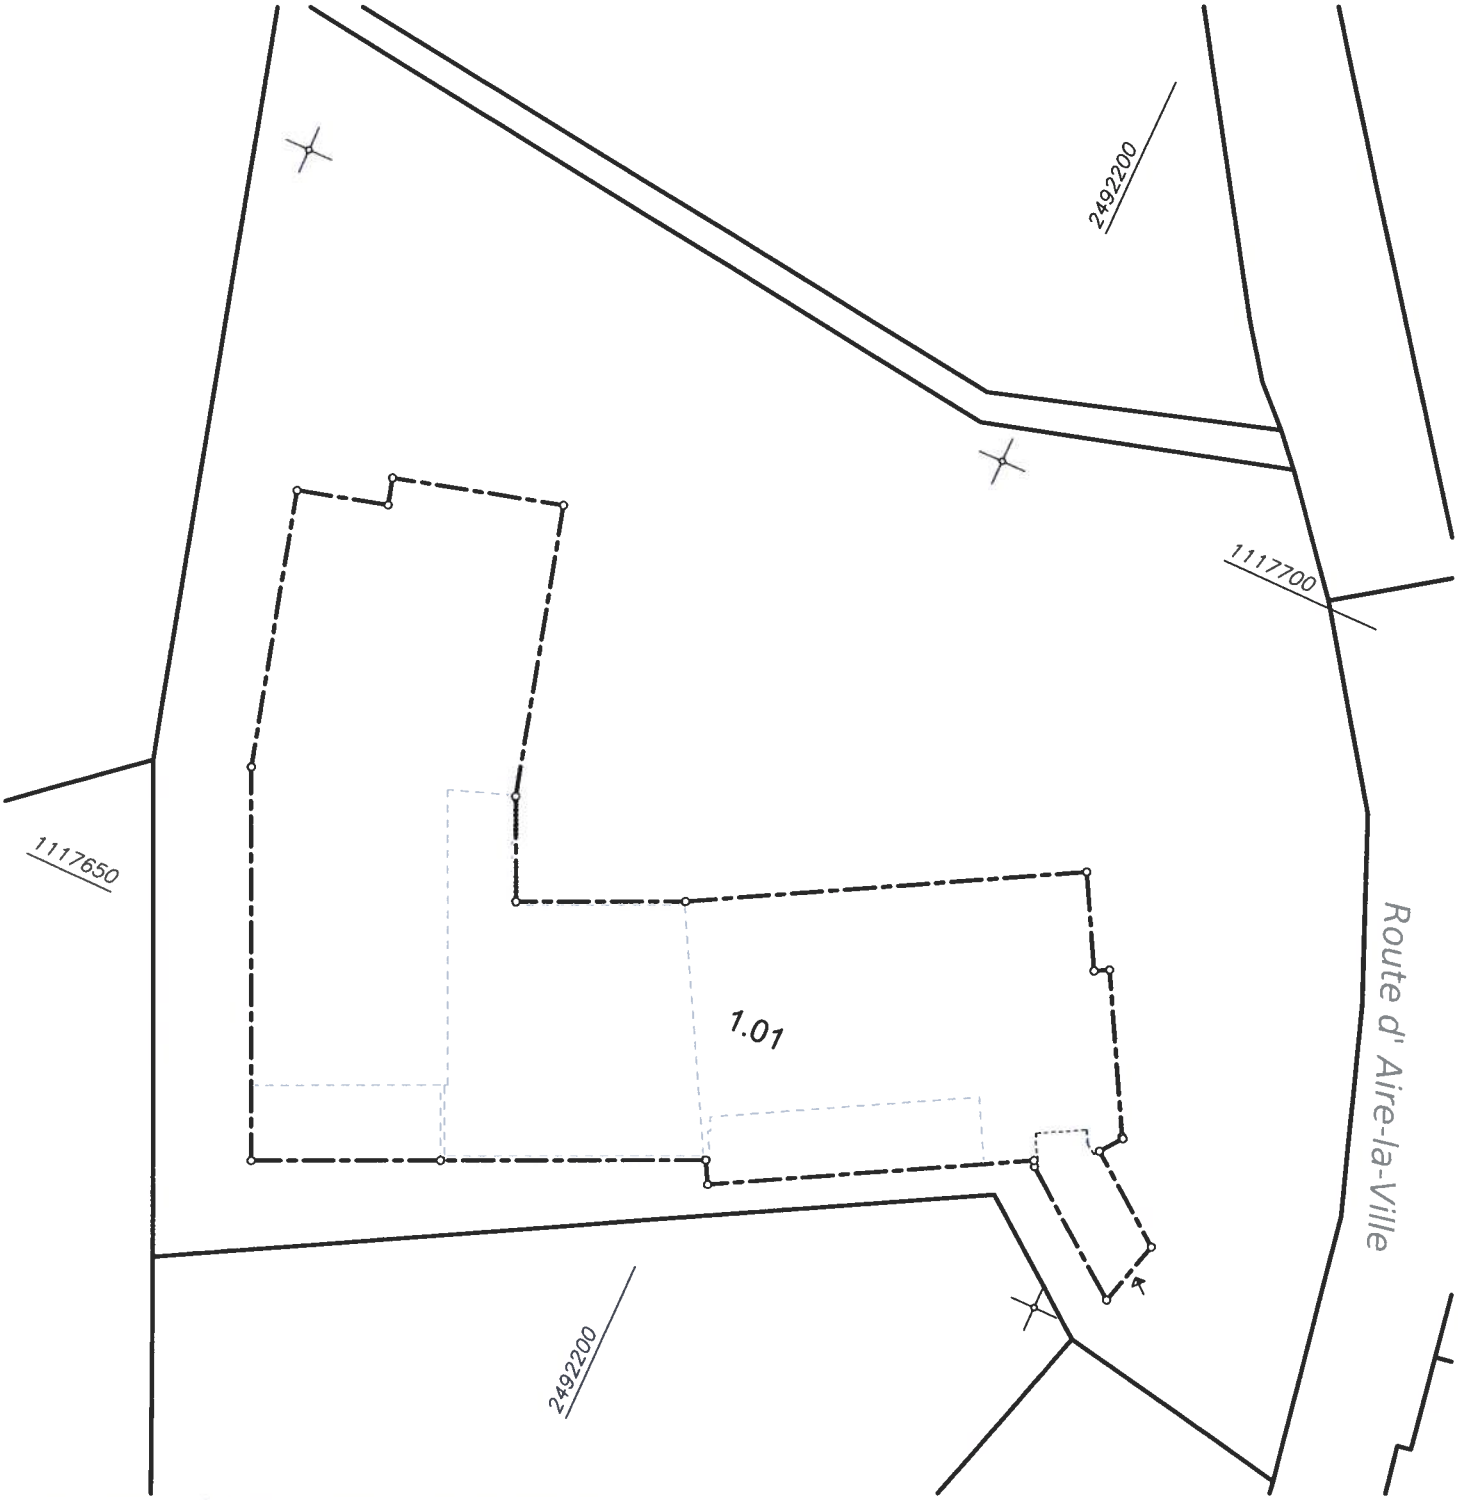

Plan de répartition des locaux

KÜPFER GÉOMÈTRES SA
INGÉNIEUR GÉOMÈTRE OFFICIEL EPF/AGG
RUE EUGÈNE-MARZIANO 41
CH 1227 LES ACACIAS
TEL 022 732 03 12
kupfer-geometre.ch
akupfer@worldcom.ch

Dossier : 2794 / GDC

Bâtiment	:	Projet
Niveau (entresol)	:	2
Echelle	:	1:500
Date	:	03.03.2023
Dernière modif.	:	22.11.2023

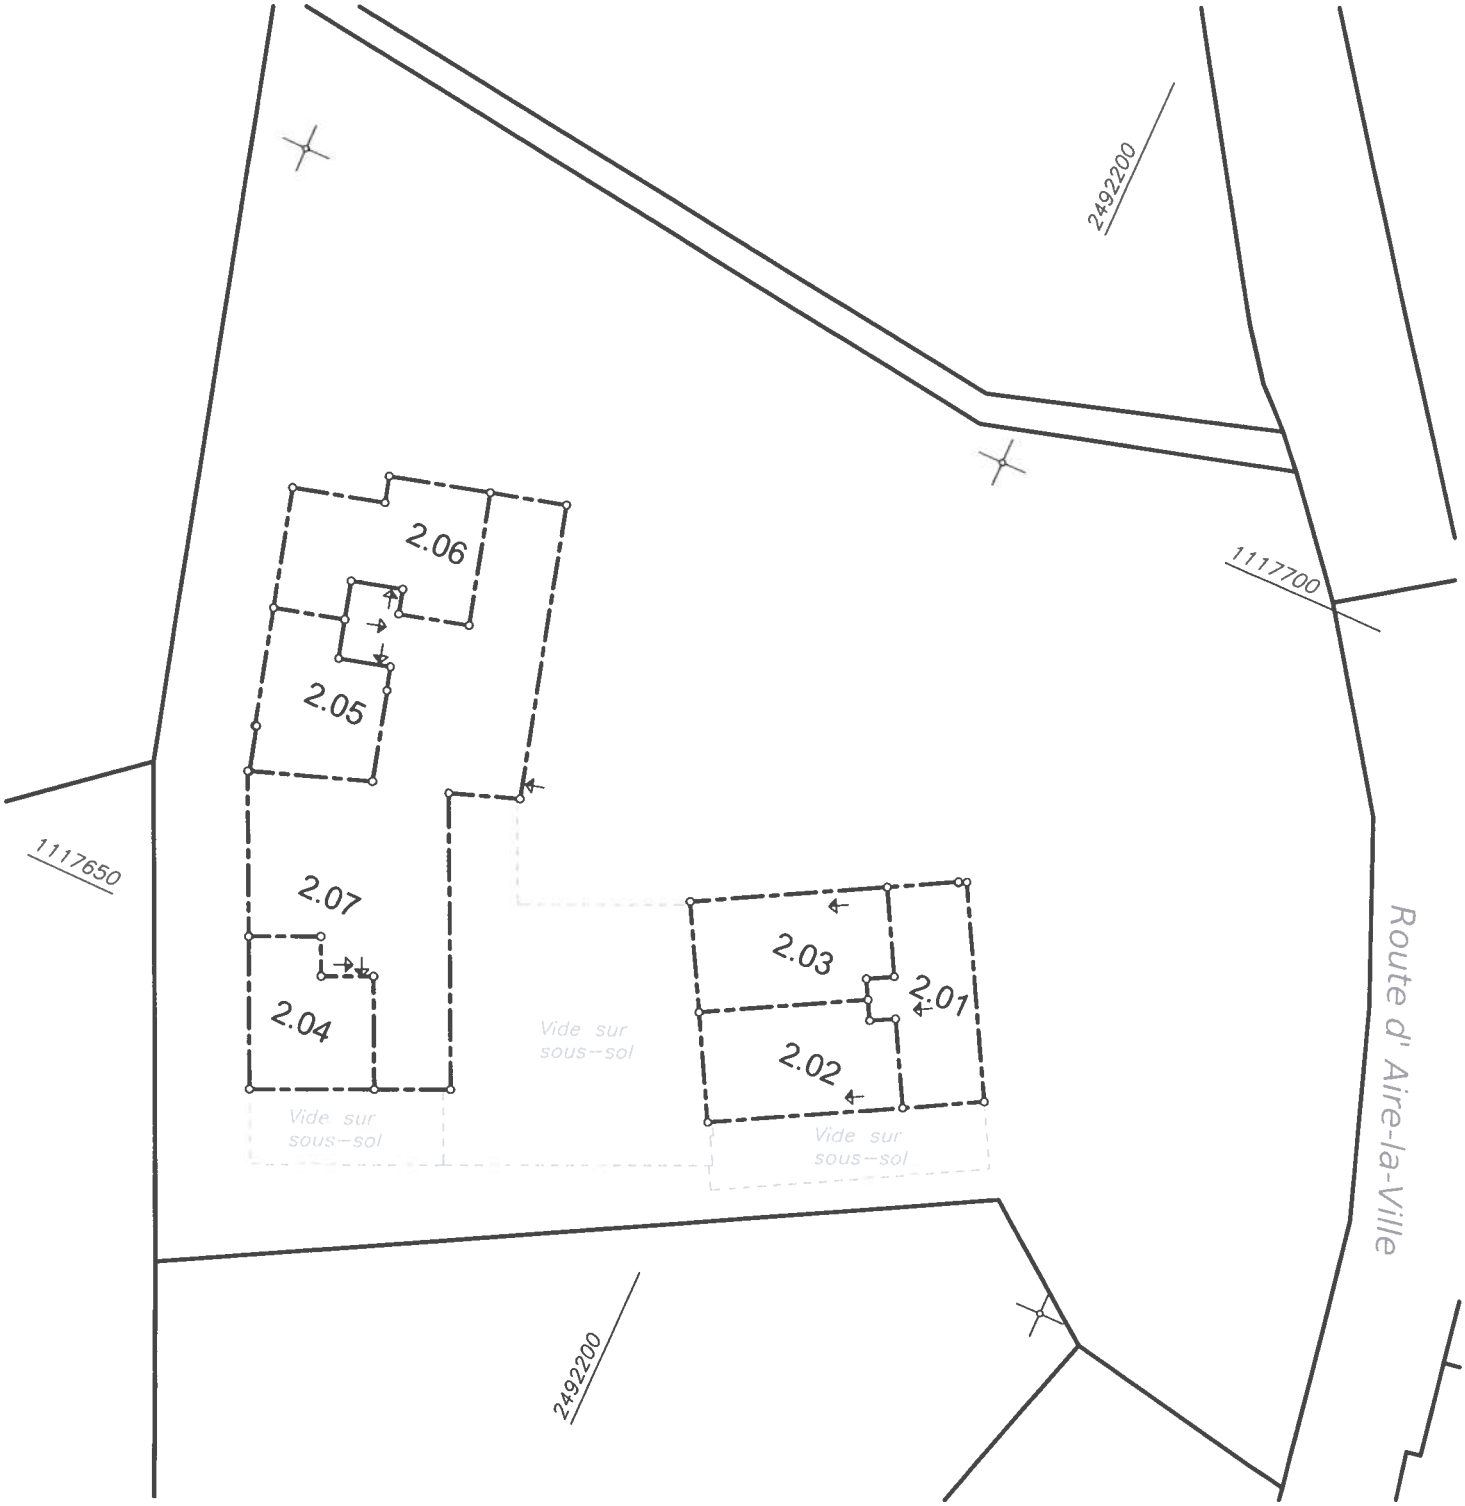

Plan de répartition des locaux

KÜPFER GÉOMÈTRES SA
INGÉNIEUR GÉOMÈTRE OFFICIEL EPF/AGG
RUE EUGÈNE-MARZIANO 41
CH 1227 LES ACACIAS
TEL 022 732 03 12
kupfer-geometre.ch
akupfer@worldcom.ch

Dossier : 2794 / GDC

Bâtiment	:	Projet
Niveau (rez-de-chaussée)	:	3
Echelle	:	1:500
Date	:	03.03.2023
Dernière modif.	:	-

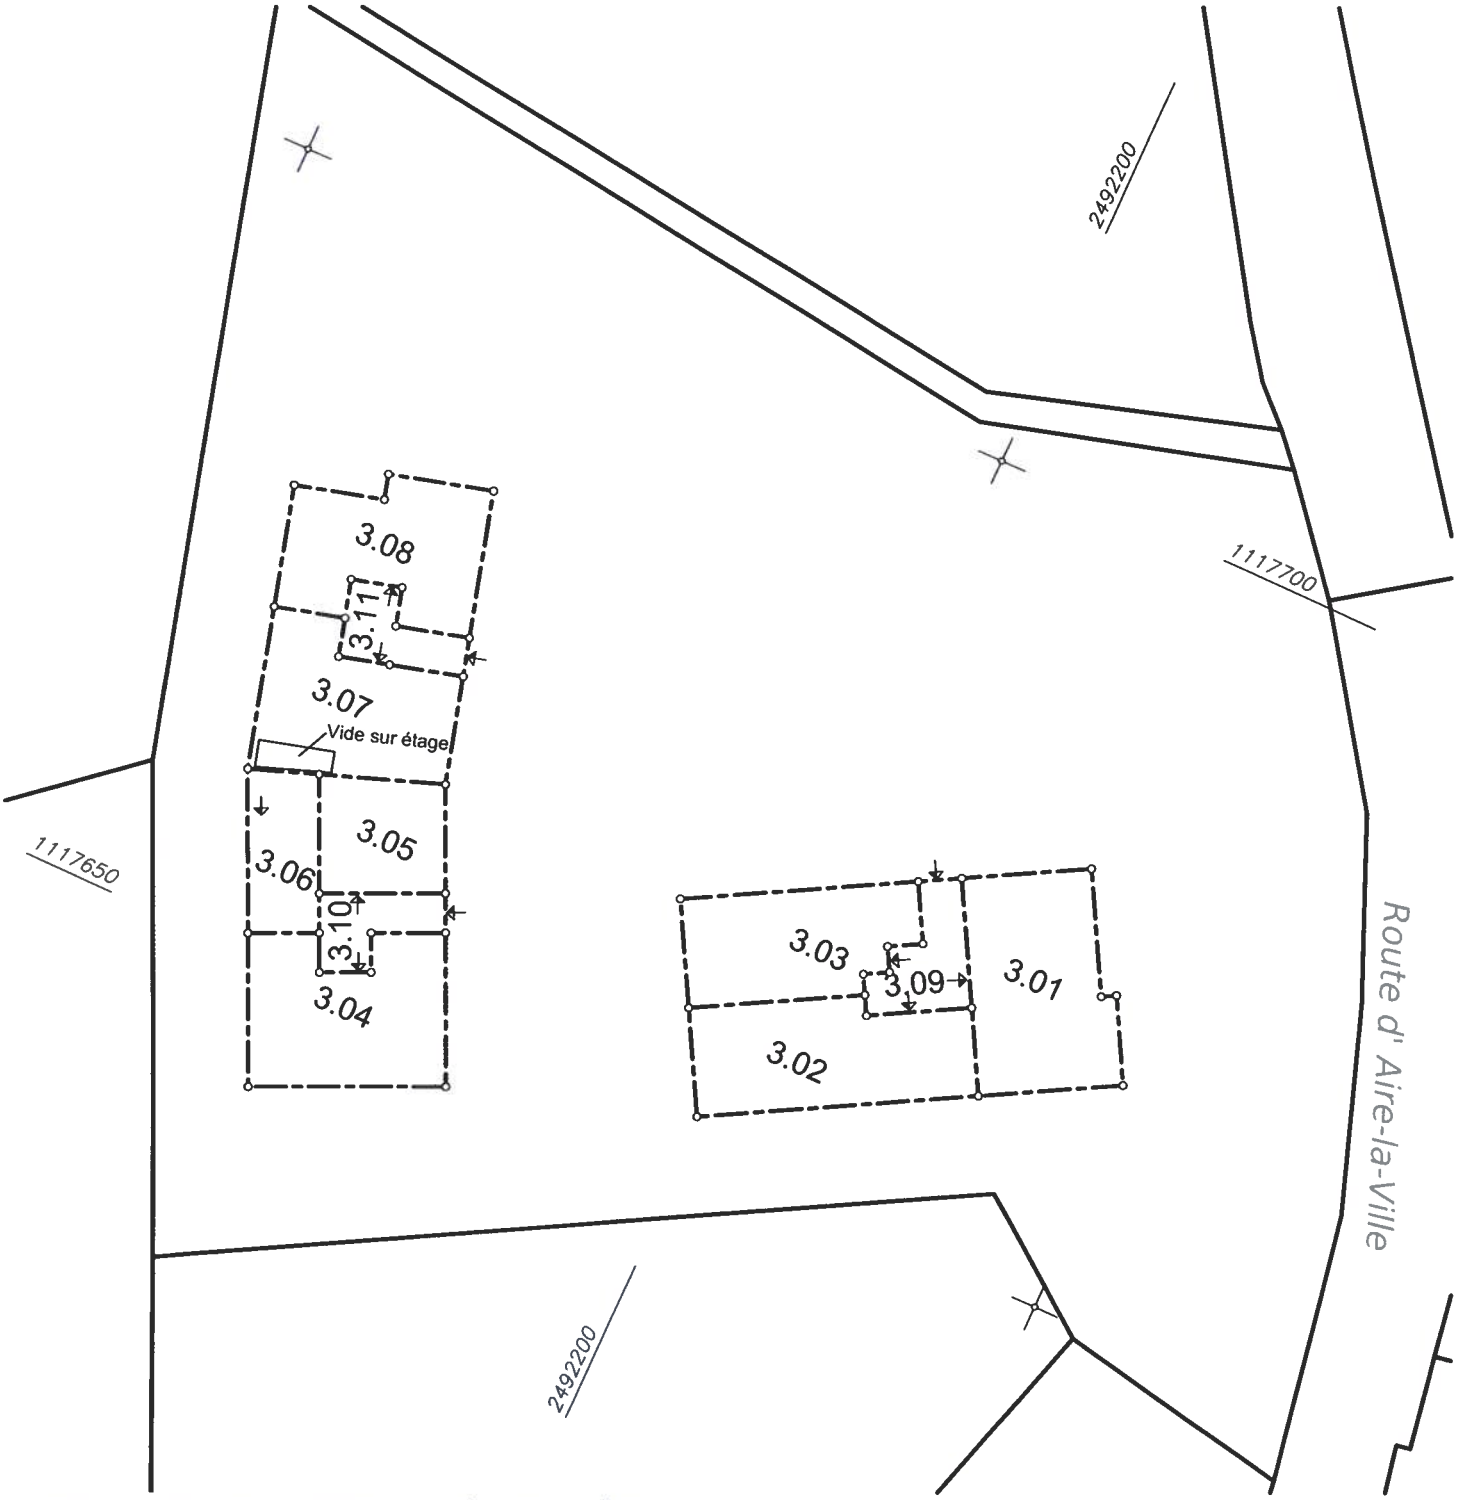

Plan de répartition des locaux

KÜPFER GÉOMÈTRES SA
INGÉNIEUR GÉOMÈTRE OFFICIEL EPF/AGG
RUE EUGÈNE-MARZIANO 41
CH 1227 LES ACACIAS
TEL 022 732 03 12
kupfer-geometre.ch
akupfer@worldcom.ch

Dossier : 2794 / GDC

Bâtiment	:	Projet
Niveau	:	4
(1er étage)		
Echelle	:	1:500
Date	:	03.03.2023
Dernière modif.	:	-

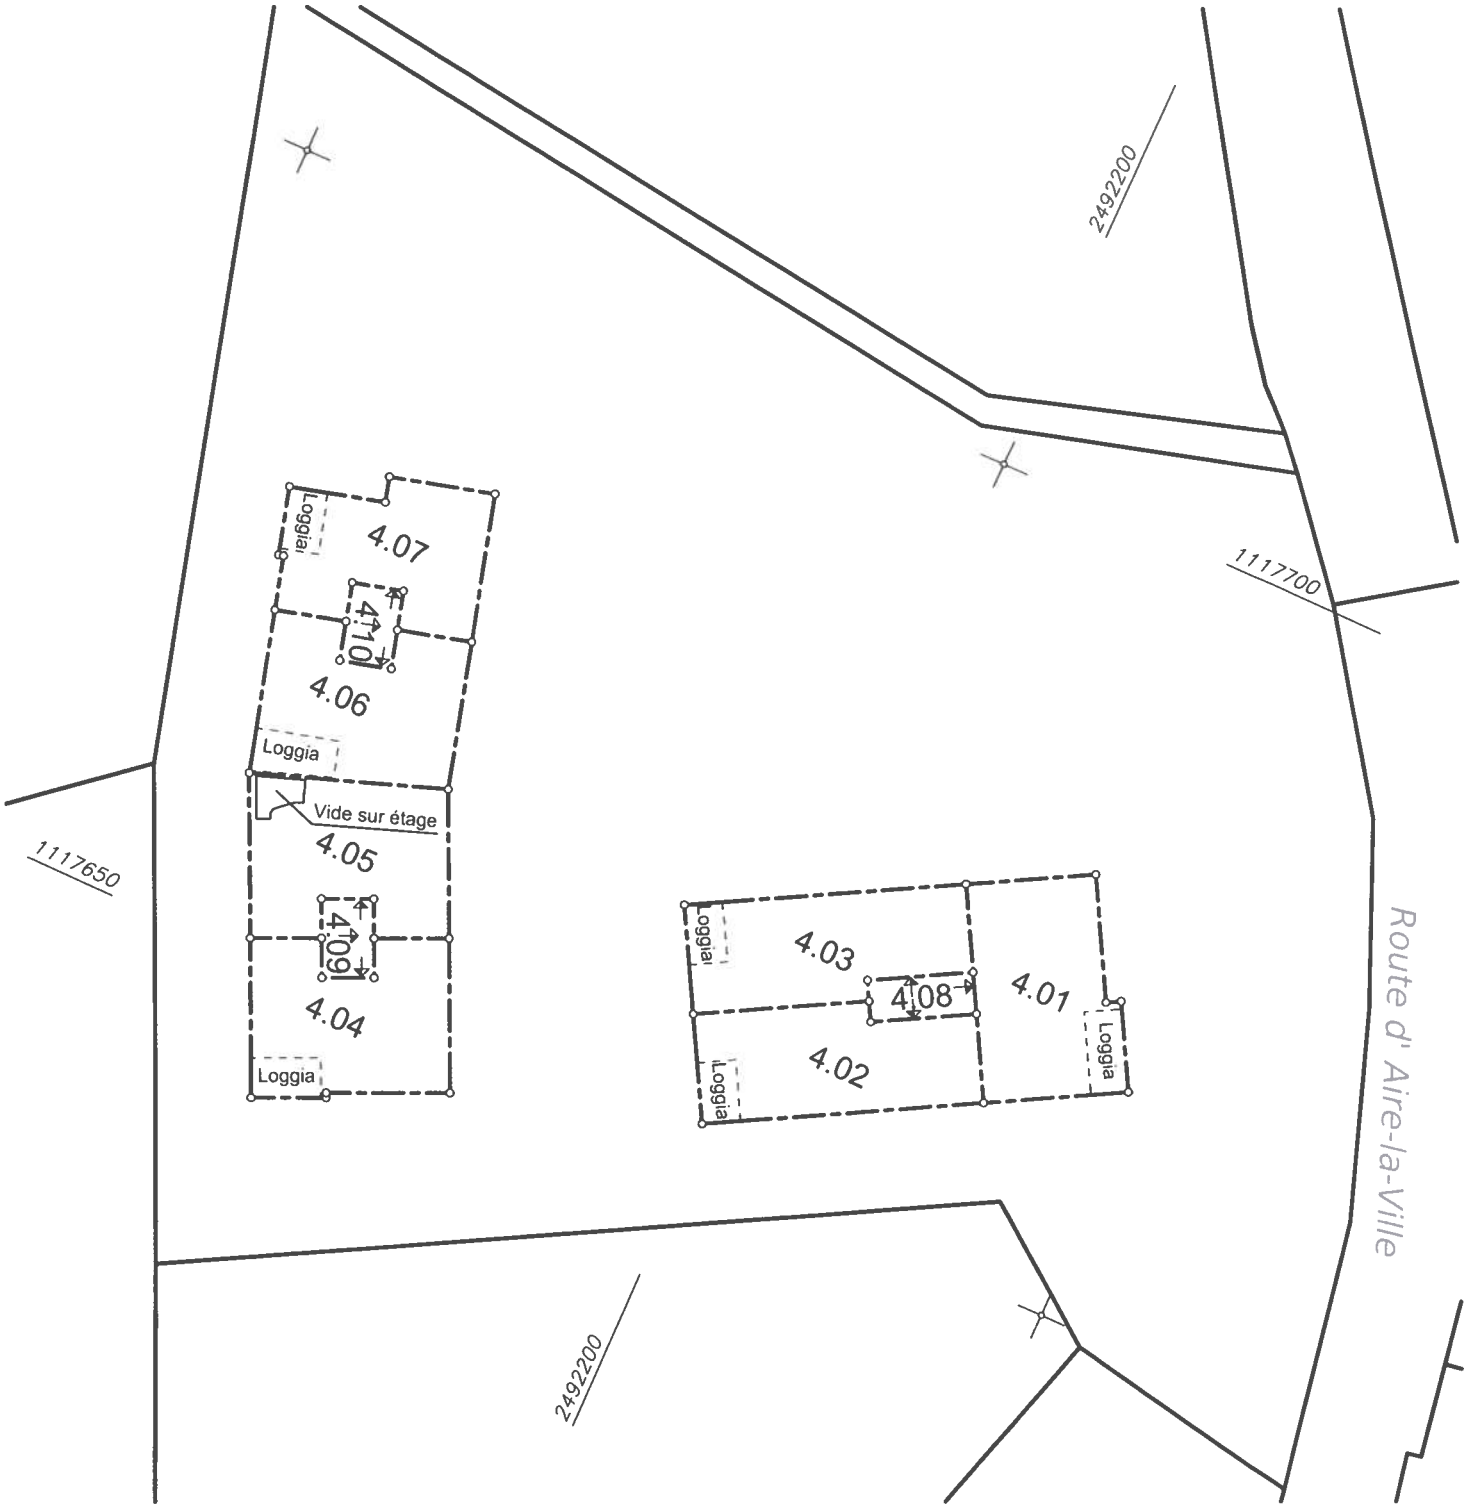

Plan de répartition des locaux

KÜPFER GÉOMÈTRES SA
INGÉNIEUR GÉOMÈTRE OFFICIEL EPF/AGG
RUE EUGÈNE-MARZIANO 41
CH 1227 LES ACACIAS
TEL 022 732 03 12
kupfer-geometre.ch
akupfer@worldcom.ch

Dossier : 2794 / GDC

Bâtiment	:	Projet
Niveau	:	5
(2ème étage)		
Echelle	:	1:500
Date	:	03.03.2023
Dernière modif.	:	-

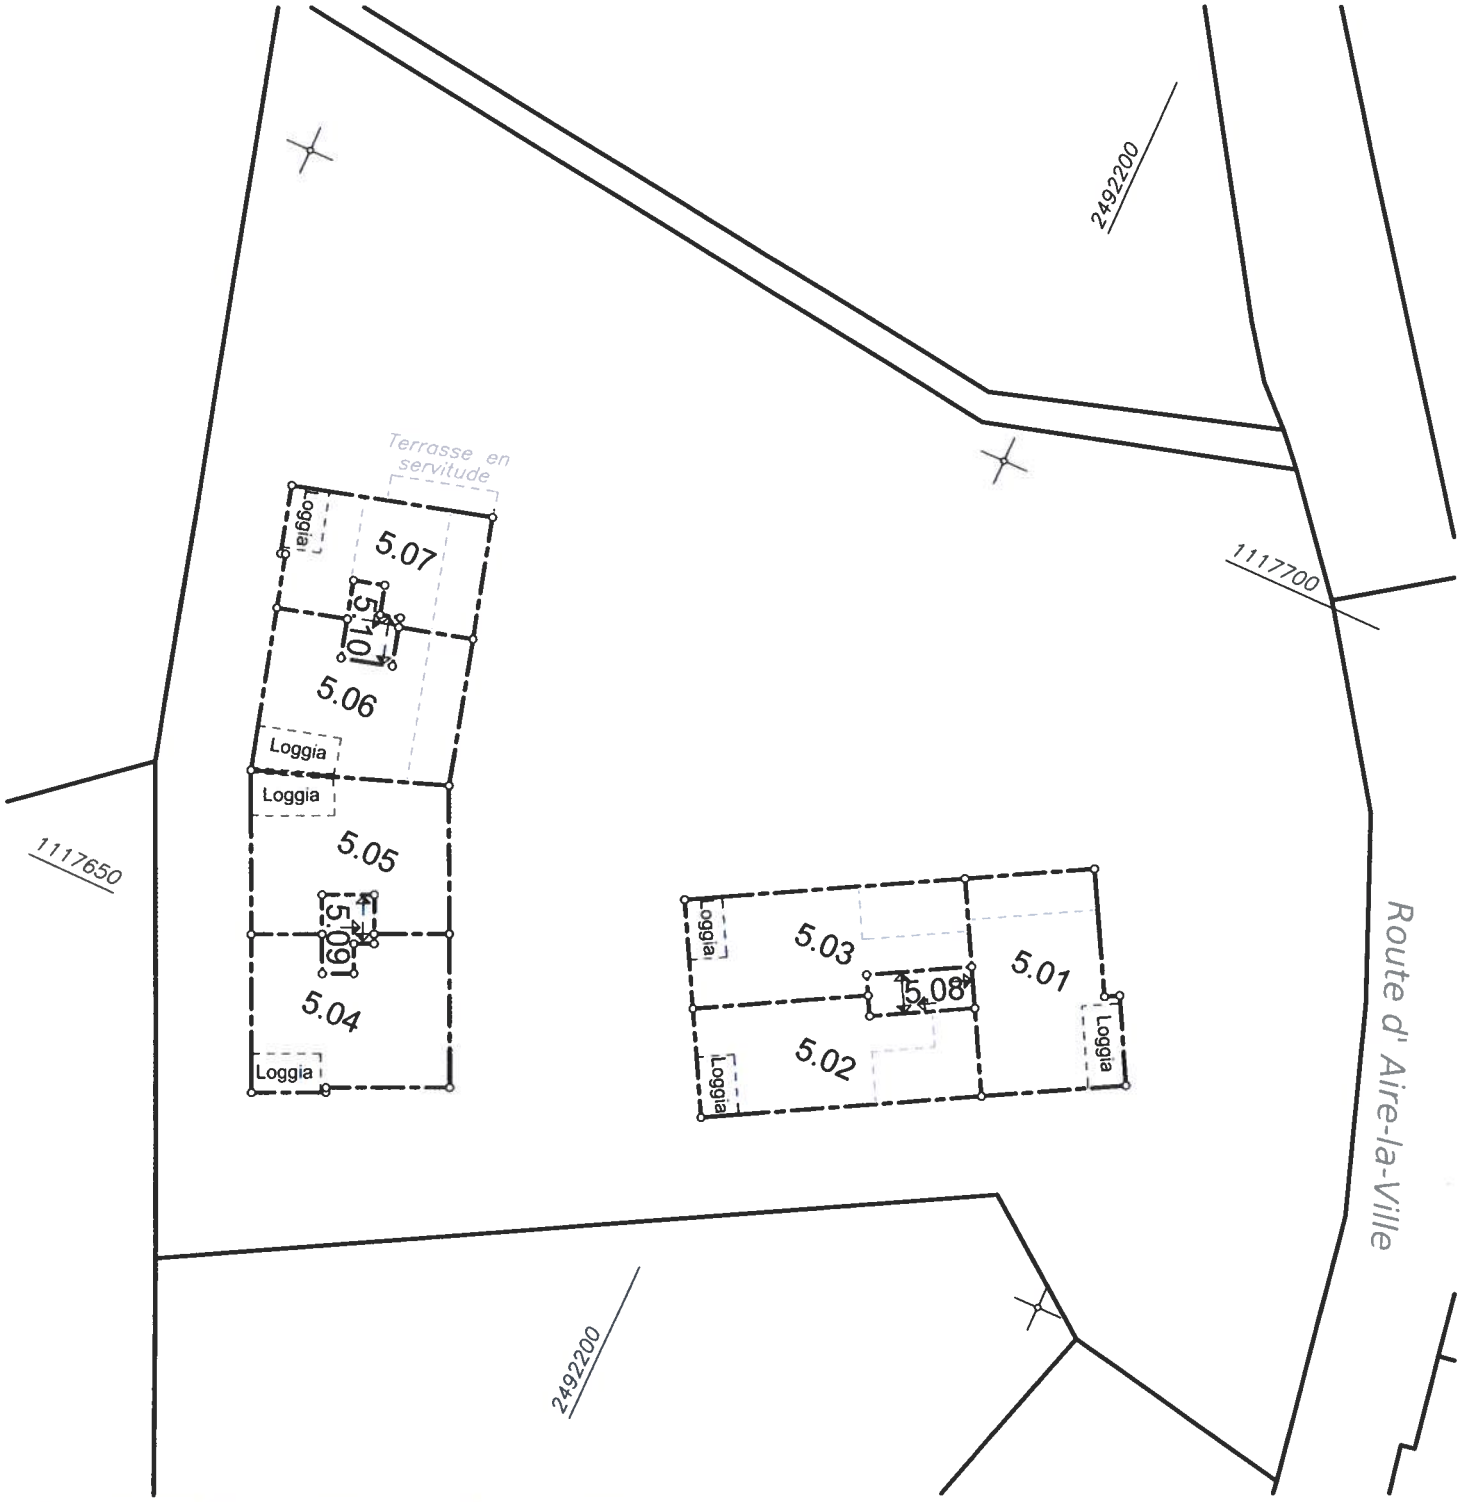

Plan de répartition des locaux

KÜPFER GÉOMÈTRES SA
INGÉNIEUR GÉOMÈTRE OFFICIEL EPF/AGG
RUE EUGÈNE-MARZIANO 41
CH 1227 LES ACACIAS
TEL 022 732 03 12
kupfer-geometre.ch
akupfer@worldcom.ch

Dossier : 2794 / GDC

Bâtiment	:	Projet
Niveau (mezzanine)	:	6
Echelle	:	1:250
Date	:	03.03.2023
Dernière modif.	:	-

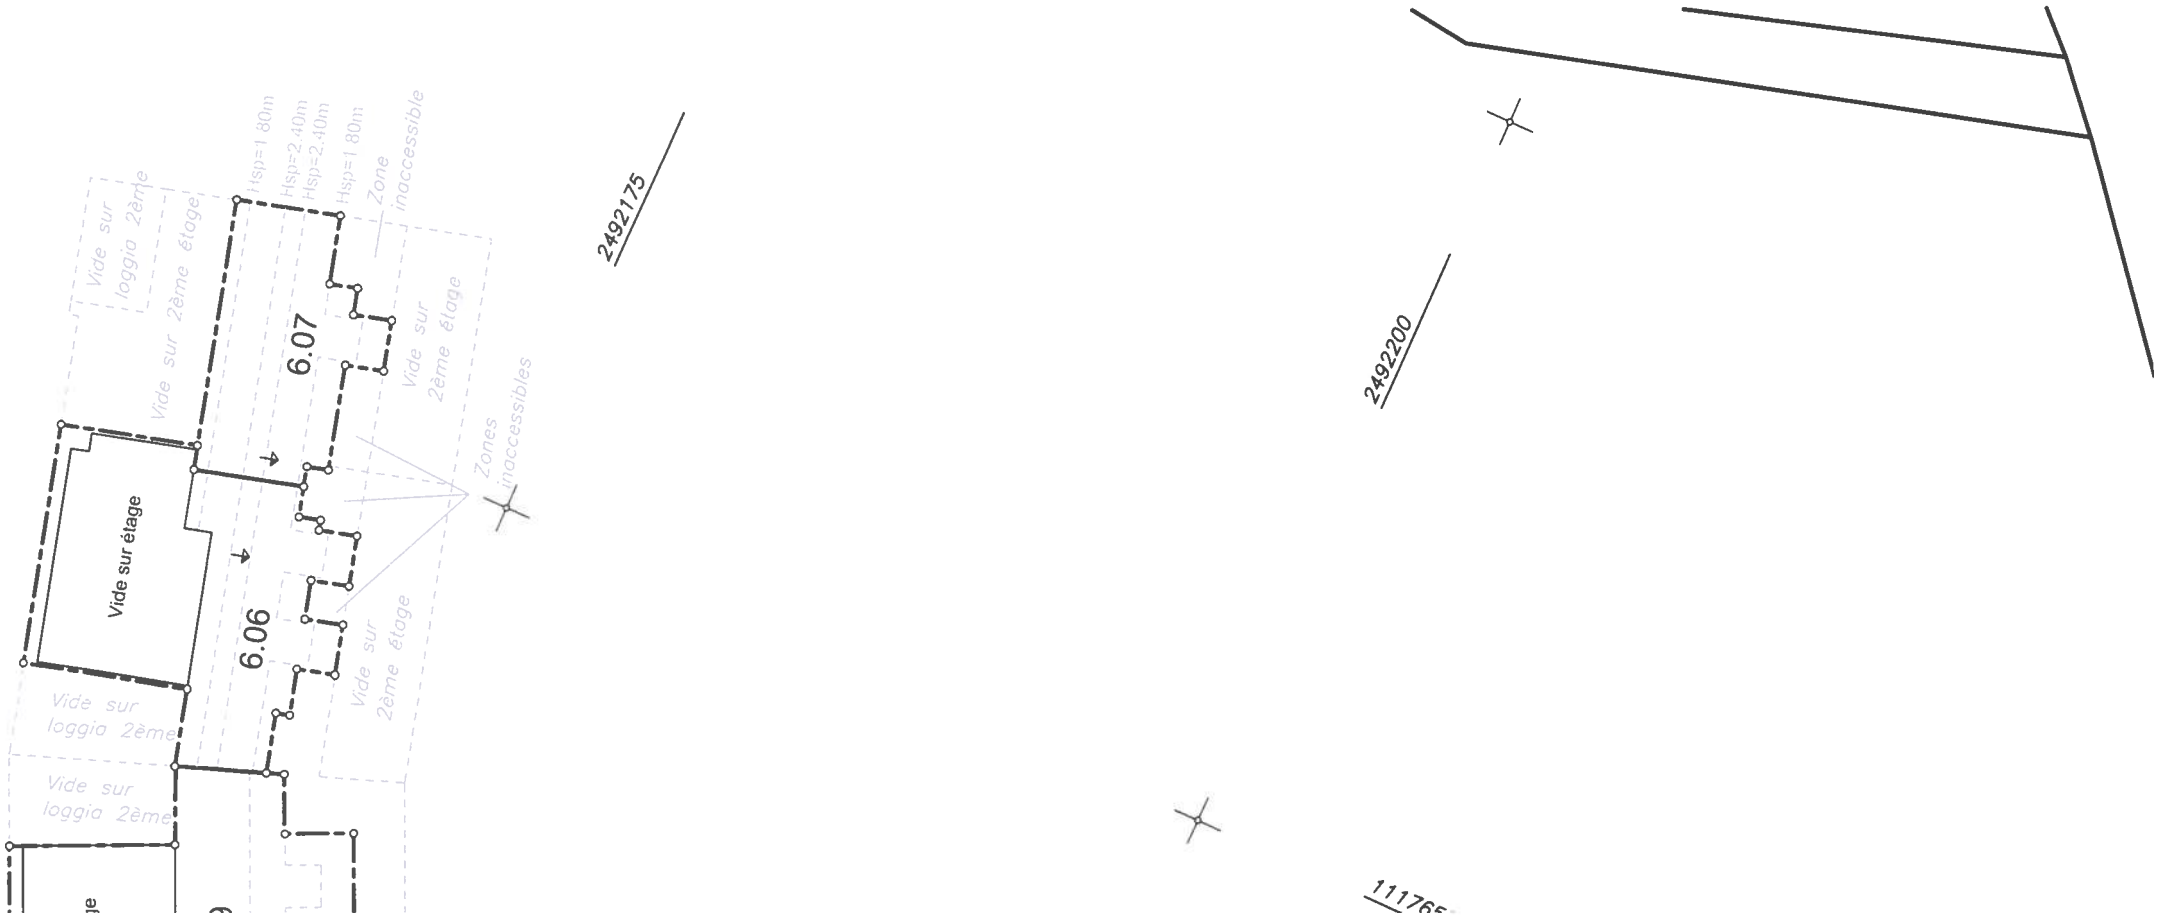

TABLEAU DE RÉPARTITION DES LOCAUX

Commune : Satigny
Section :
Immeuble : 7177 **Mutation :** 1/2023

Plan page	Valeurs en °/°°	Désignation Niveau	Désignation Partie	LOCAUX	Surfaces m²	OBSERVATIONS (*)	Vient de	Va à
				Sous-sol				
4	0	1	01	Accès	1519	PC		
					1519			
				Entresol				
5	0	2	01	Local	82	PC		
	10	2	02	Partie appartement	91	U1		
	10	2	03	Partie appartement	91	U2		
	8	2	04	Partie appartement	73	U3		
	8	2	05	Partie appartement	77	U4		
	10	2	06	Partie appartement	102	U5		
	0	2	07	Accès et locaux	363	PC		
					879			
				Rez-de-chaussée				
6	45	3	01	Appartement	129			
	44	3	02	Partie appartement	124	U1		
	36	3	03	Partie appartement	103	U2		
	43	3	04	Partie appartement	123	U3		
	22	3	05	Appartement	63			
	5	3	06	Partie appartement	50	U6		
	37	3	07	Partie appartement	105	U4		
	39	3	08	Partie appartement	109	U5		
	0	3	09	Accès	40	PC		
	0	3	10	Accès	31	PC		
	0	3	11	Accès	30	PC		
					907			
	317							

(*) Abréviations : DEP = Dépendance - LA = Local Annexe - PC = Partie Commune - R = Repose - U = Unité

KÜPFER GÉOMÈTRES SA
INGÉNIEUR GÉOMÈTRE OFFICIEL EPF/AGG

RUE EUGÈNE-MARZIANO 41
CH 1227 LES ACACIAS
TEL 022 732 03 12
kupfer-geometre.ch
akupfer@worldcom.ch

Dossier n° 2794
Etabli le : 03.03.2023 /GDC
Dernière modification le: 22.11.2023

nota : les millièmes de copropriété sont calculés par l'ingénieur géomètre breveté

TABLEAU DE RÉPARTITION DES LOCAUX

Commune : Satigny
Section :
Immeuble : 7177 **Mutation :** 1/2023

Plan page	Valeurs en °/°°	Désignation Niveau	Désignation Partie	LOCAUX	Surfaces m²	OBSERVATIONS (*)	Vient de	Va à
	317			**1er étage**				
7	46	4	01	Appartement	115			
				Loggia	14			
	44	4	02	Appartement	114			
				Loggia	10			
	43	4	03	Appartement	114			
				Loggia	10			
	44	4	04	Appartement	113			
				Loggia	12			
	42	4	05	Partie appartement	119	U6		
	44	4	06	Appartement	111			
				Loggia	14			
	39	4	07	Appartement	100			
				Loggia	10			
	0	4	08	Accès	19	PC		
	0	4	09	Accès	18	PC		
	0	4	10	Accès	18	PC		
					911			
				2ème étage				
8	45	5	01	Partie appartement	115	U7		
				Loggia	14			
	44	5	02	Partie appartement	114	U8		
				Loggia	10			
	45	5	03	Partie appartement	114	U9		
				Loggia	10			
	45	5	04	Partie appartement	115	U10		
				Loggia	12			
	44	5	05	Partie appartement	111	U11		
				Loggia	14			
	44	5	06	Partie appartement	112	U12		
				Loggia	14			
	36	5	07	Partie appartement	91	U13		
				Loggia	10			
	0	5	08	Accès	19	PC		
	0	5	09	Accès	15	PC		
	0	5	10	Accès	15	PC		
					905			
	922							

(*) Abréviations : DEP = Dépendance - LA = Local Annexe - PC = Partie Commune - R = Repose - U = Unité

KÜPFER GÉOMÈTRES SA
INGÉNIEUR GÉOMÈTRE OFFICIEL EPF/AGG

RUE EUGÈNE-MARZIANO 41
CH 1227 LES ACACIAS
TEL 022 732 03 12
kupfer-geometre.ch
akupfer@worldcom.ch

Dossier n° 2794
Etabli le : 03.03.2023 /GDC
Dernière modification le:

nota : les millièmes de copropriété sont calculés par l'ingénieur géomètre breveté

TABLEAU DE RÉPARTITION DES LOCAUX

Commune : Satigny
Section :
Immeuble : 7177 **Mutation :** 1/2023

Plan page	Valeurs en °/°°	Désignation Niveau	Désignation Partie	LOCAUX	Surfaces m²	OBSERVATIONS (*)	Vient de	Va à
	922							
				Mezzanine				
9	15	6	01	Partie appartement	35	U7		
				Sous-pentes<2.40m	10			
				Sous-pentes<1.80m	16			
	9	6	02	Partie appartement	15	U8		
				Sous-pentes<2.40m	15			
				Sous-pentes<1.80m	14			
	9	6	03	Partie appartement	15	U9		
				Sous-pentes<2.40m	15			
				Sous-pentes<1.80m	13			
9	17	6	04	Partie appartement	31	U10		
				Sous-pentes<2.40m	26			
				Sous-pentes<1.80m	10			
	13	6	05	Partie appartement	25	U11		
				Sous-pentes<2.40m	19			
				Sous-pentes<1.80m	13			
	8	6	06	Partie appartement	6	U12		
				Sous-pentes<2.40m	28			
				Sous-pentes<1.80m	9			
	7	6	07	Partie appartement	6	U13		
				Sous-pentes<2.40m	22			
				Sous-pentes<1.80m	10			
		6	08	Local	23	PC		
					228			
	1000							

(*) Abréviations : DEP = Dépendance - LA = Local Annexe - PC = Partie Commune - R = Repose - U = Unité

KÜPFER GÉOMÈTRES SA
INGÉNIEUR GÉOMÈTRE OFFICIEL EPF/AGG

RUE EUGÈNE-MARZIANO 41
CH 1227 LES ACACIAS
TEL 022 732 03 12
kupfer-geometre.ch
akupfer@worldcom.ch

Dossier n° 2794
Etabli le : 03.03.2023 /GDC
Dernière modification le:

nota : les millièmes de copropriété sont calculés par l'ingénieur géomètre breveté

TABLEAU RÉCAPITULATIF

Commune : Satigny
Section :
Immeuble : 7177 **Mutation :** 1/2023

Feuillet R.F.	Valeurs en °/°°	Lots	LOCAUX	ETAGE	OBSERVATIONS (*)	Vient de	Va à
101	45	3.01	Appartement	Rez-de-chaussée			
102	54	2.02	Partie appartement	Entresol	U1		
		3.02	Partie appartement	Rez-de-chaussée			
103	46	2.03	Partie appartement	Entresol	U2		
		3.03	Partie appartement	Rez-de-chaussée			
104	51	2.04	Partie appartement	Entresol	U3		
		3.04	Partie appartement	Rez-de-chaussée			
105	22	3.05	Appartement	Rez-de-chaussée			
106	45	2.05	Partie appartement	Entresol	U4		
		3.07	Partie appartement	Rez-de-chaussée			
107	49	2.06	Partie appartement	Entresol	U5		
		3.08	Partie appartement	Rez-de-chaussée			
108	46	4.01	Appartement	1er étage			
			Loggia				
109	47	3.06	Partie appartement	Rez-de-chaussée	U6		
		4.05	Partie appartement	1er étage			
110	60	5.01	Partie appartement	2ème étage	U7		
			Loggia				
		6.01	Partie appartement	Mezzanine			
			Sous-pentes<2.40m				
			Sous-pentes<1.80m				
111	44	4.02	Appartement	1er étage			
			Loggia				
112	43	4.03	Appartement	1er étage			
			Loggia				
	552						

(*) Abréviations : DEP = Dépendance - LA = Local Annexe - PC = Partie Commune - R = Repose - U = Unité

KÜPFER GÉOMÈTRES SA
INGÉNIEUR GÉOMÈTRE OFFICIEL EPF/AGG

RUE EUGÈNE-MARZIANO 41
CH 1227 LES ACACIAS
TEL 022 732 03 12
kupfer-geometre.ch
akupfer@worldcom.ch

Dossier n° 2794
Etabli le : 03.03.2023 /GDC
Dernière modification le:

nota : les millièmes de copropriété sont calculés par l'ingénieur géomètre breveté

TABLEAU RÉCAPITULATIF

Commune : Satigny
Section :
Immeuble : 7177 **Mutation :** 1/2023

Feuillet R.F.	Valeurs en °/°°	Lots	LOCAUX	ETAGE	OBSERVATIONS (*)	Vient de	Va à
	552						
113	44	4.04	Appartement Loggia	1er étage			
114	44	4.06	Appartement Loggia	1er étage			
115	39	4.07	Appartement Loggia	1er étage			
116	53	5.02 6.02	Partie appartement Loggia Partie appartement Sous-pentes<2.40m Sous-pentes<1.80m	2ème étage Mezzanine	U8		
117	54	5.03 6.03	Partie appartement Loggia Partie appartement Sous-pentes<2.40m Sous-pentes<1.80m	2ème étage Mezzanine	U9		
118	62	5.04 6.04	Partie appartement Loggia Partie appartement Sous-pentes<2.40m Sous-pentes<1.80m	2ème étage Mezzanine	U10		
119	57	5.05 6.05	Partie appartement Loggia Partie appartement Sous-pentes<2.40m Sous-pentes<1.80m	2ème étage Mezzanine	U11		
	905						

(*) Abréviations : DEP = Dépendance - LA = Local Annexe - PC = Partie Commune - R = Repose - U = Unité

KÜPFER GÉOMÈTRES SA
INGÉNIEUR GÉOMÈTRE OFFICIEL EPF/AGG

RUE EUGÈNE-MARZIANO 41
CH 1227 LES ACACIAS
TEL 022 732 03 12
kupfer-geometre.ch
akupfer@worldcom.ch

Dossier n° 2794
Etabli le : 03.03.2023 /GDC
Dernière modification le:

nota : les millièmes de copropriété sont calculés par l'ingénieur géomètre breveté

TABLEAU RÉCAPITULATIF

Commune : Satigny
Section :
Immeuble : 7177 **Mutation :** 1/2023

Feuillet R.F.	Valeurs en °/°°	Lots	LOCAUX	ETAGE	OBSERVATIONS (*)	Vient de	Va à
	905						
120	52	5.06	Partie appartement Loggia	2ème étage	U12		
		6.06	Partie appartement Sous-pentes<2.40m Sous-pentes<1.80m	Mezzanine			
121	43	5.07	Partie appartement Loggia	2ème étage	U13		
		6.07	Partie appartement Sous-pentes<2.40m Sous-pentes<1.80m	Mezzanine			
	1000						

(*) Abréviations : DEP = Dépendance - LA = Local Annexe - PC = Partie Commune - R = Repose - U = Unité

KÜPFER GÉOMÈTRES SA
INGÉNIEUR GÉOMÈTRE OFFICIEL EPF/AGG

RUE EUGÈNE-MARZIANO 41
CH 1227 LES ACACIAS
TEL 022 732 03 12
kupfer-geometre.ch
akupfer@worldcom.ch

Dossier n° 2794
Etabli le : 03.03.2023 /GDC
Dernière modification le:

nota : les millièmes de copropriété sont calculés par l'ingénieur géomètre breveté

Plan de servitude

Annexe 1

KÜPFER GÉOMÈTRES SA
INGÉNIEUR GÉOMÈTRE OFFICIEL EPF/AGG
RUE EUGÈNE-MARZIANO 41
CH 1227 LES ACACIAS
TEL 022 732 03 12
kupfer-geometre.ch
akupfer@worldcom.ch

Dossier : 2794 / GDC

Bâtiment	:	Projet
Niveau (sous-sol)	:	1
Echelle	:	1:500
Date	:	03.03.2023
Dernière modif.	:	05.03.2024
Visa	:	

Provisoire à l'examen

- USAGE : Usage de places de stationnement 13 à 17 – 22 à 30 – 33 à 39
- USAGE : Usage de places de stationnement (motos) M1 à M6
- USAGE : Usage de box 1 à 4, 5a, 5b et 6 à 9
- USAGE : Usage de caves 1 à 3 et 20–21

Plan de servitude

Annexe 2

KÜPFER GÉOMÈTRES SA
INGÉNIEUR GÉOMÈTRE OFFICIEL EPF/AGG
RUE EUGÈNE-MARZIANO 41
CH 1227 LES ACACIAS
TEL 022 732 03 12
kupfer-geometre.ch
akupfer@worldcom.ch

Dossier : 2794 / GDC

Bâtiment	:	Projet
Niveau (entresol)	:	2
Echelle	:	1:500
Date	:	03.03.2023
Dernière modif.	:	22.11.2023
Visa	:	

Provisoire à l'examen

USAGE : Usage de caves 4, 5, 6, 8, 10, 11, 12, 13, 15 à 19 et 22 à 25

Plan de servitude

Annexe 3

KÜPFER GÉOMÈTRES SA
INGÉNIEUR GÉOMÈTRE OFFICIEL EPF/AGG
RUE EUGÈNE-MARZIANO 41
CH 1227 LES ACACIAS
TEL 022 732 03 12
kupfer-geometre.ch
akupfer@worldcom.ch

Dossier : 2794 / GDC

Bâtiment	:	Projet
Niveau (rez-de-chaussée)	:	3
Echelle	:	1:500
Date	:	03.03.2023
Dernière modif.	:	15.12.2023
Visa	:	

Provisoire à l'examen

USAGE : Usage de jardins et de terrasses J1 à J9

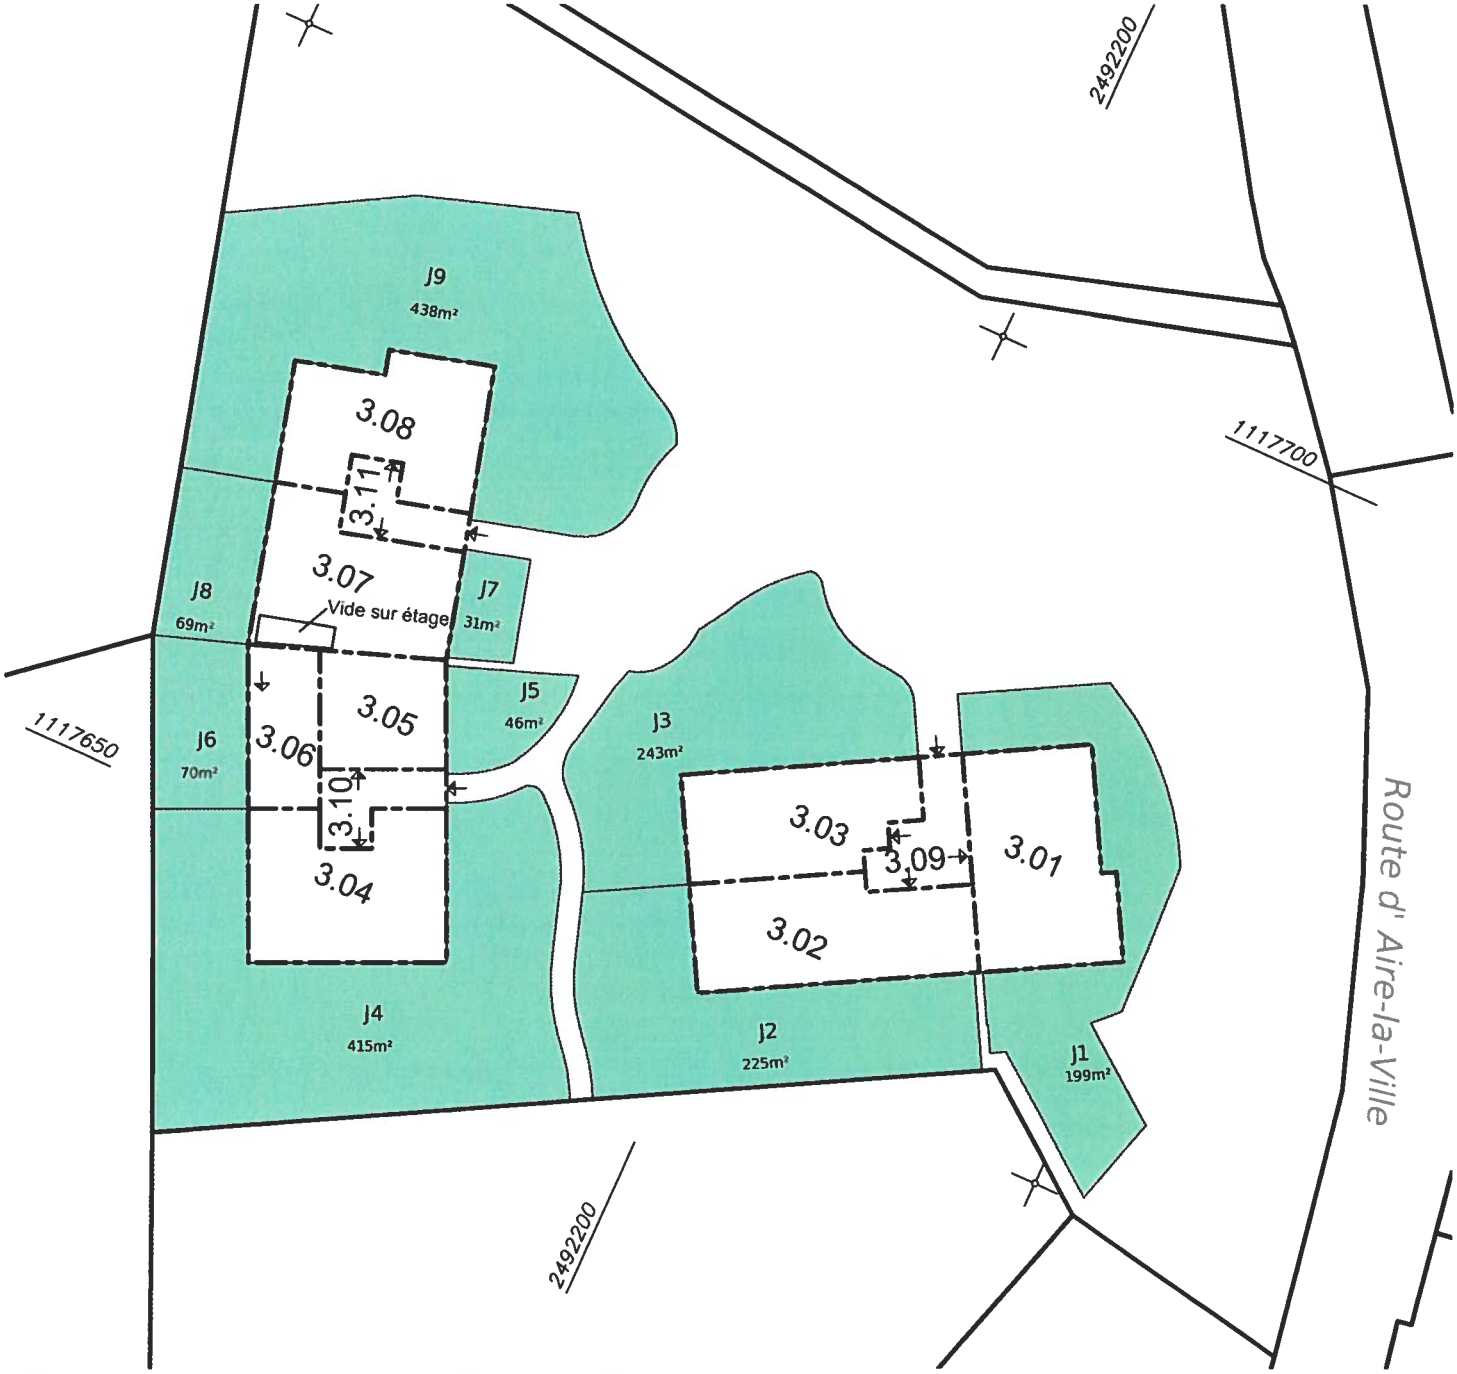

Plan de servitude

Annexe 4

KÜPFER GÉOMÈTRES SA
INGÉNIEUR GÉOMÈTRE OFFICIEL EPF/AGG
RUE EUGÈNE-MARZIANO 41
CH 1227 LES ACACIAS
TEL 022 732 03 12
kupfer-geometre.ch
akupfer@worldcom.ch

Dossier : 2794 / GDC

Bâtiment	:	Projet
Niveau	:	5
(2ème étage)		
Echelle	:	1:500
Date	:	03.03.2023
Dernière modif.	:	-
Visa	:	

Provisoire à l'examen

USAGE : Usage de terrasse T11

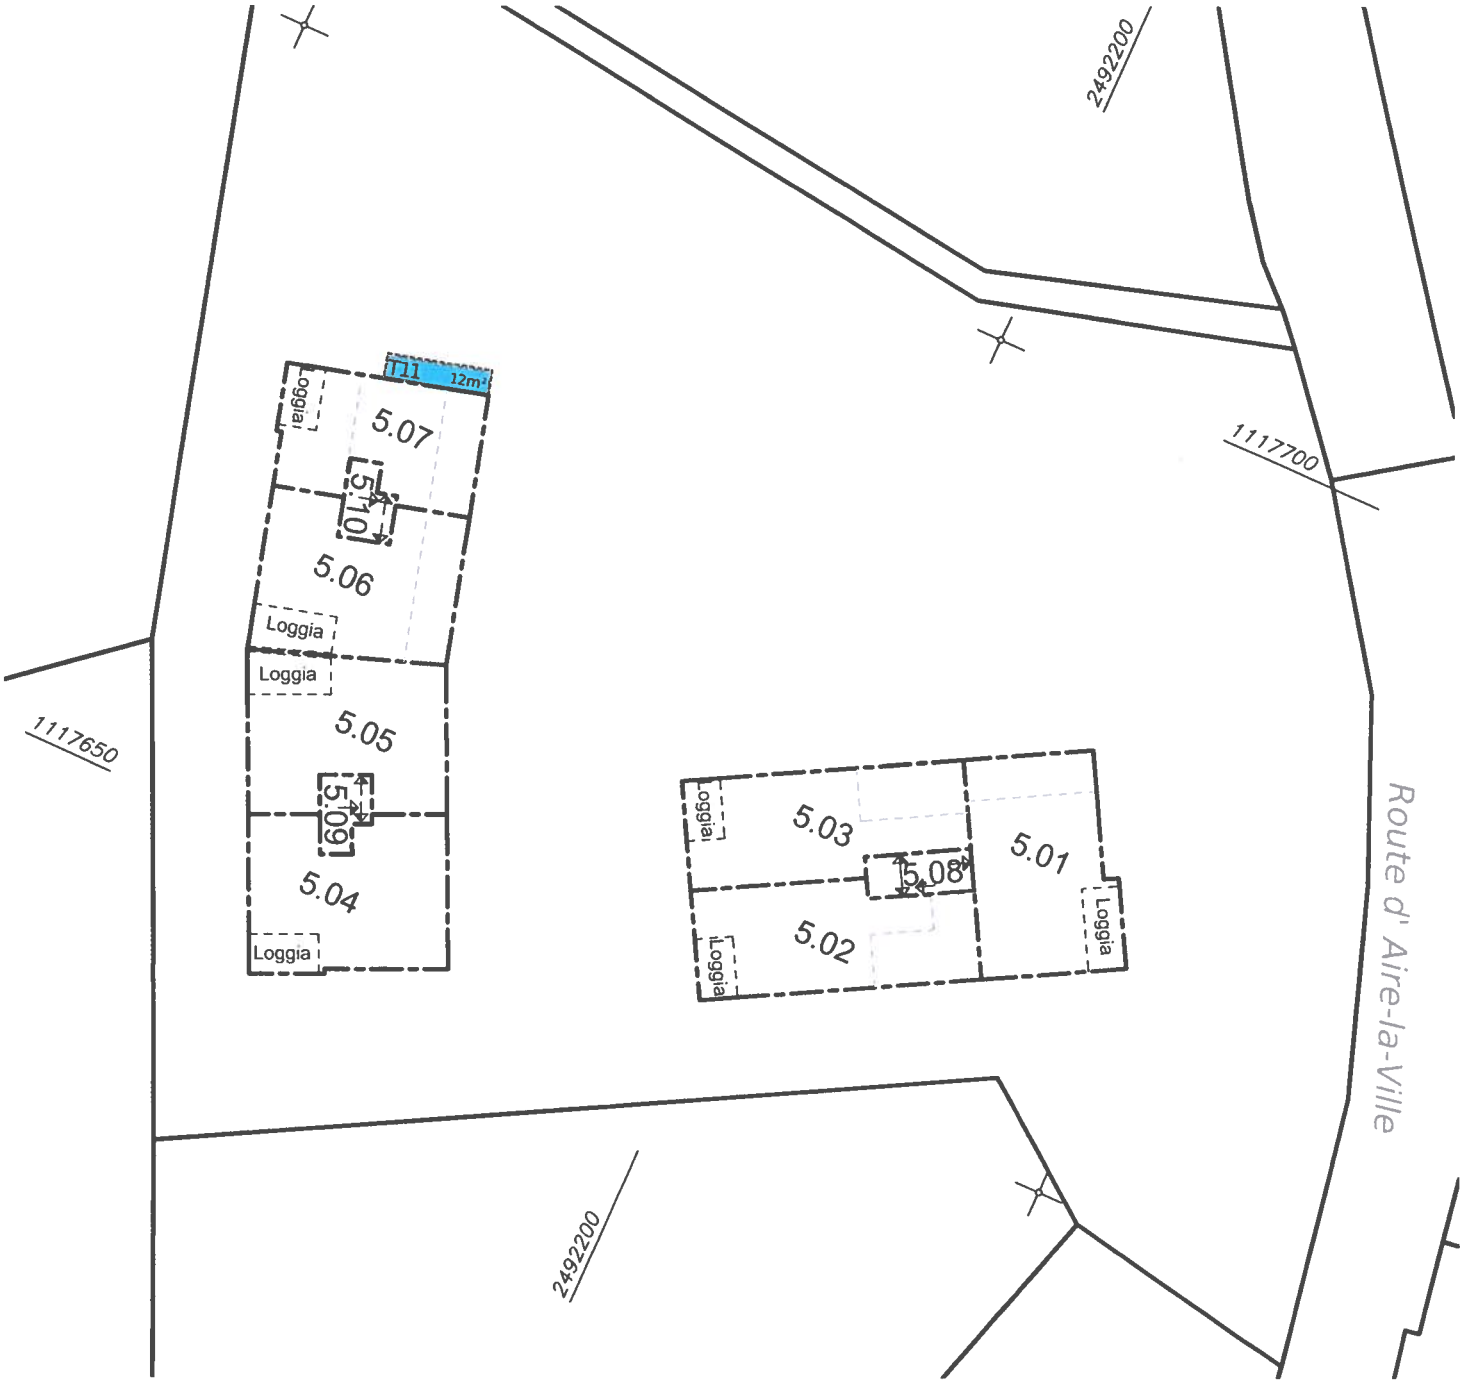

Plan de servitude

KÜPFER GÉOMÈTRES SA
INGÉNIEUR GÉOMÈTRE OFFICIEL EPF/AGG
RUE EUGÈNE-MARZIANO 41
CH 1227 LES ACACIAS
TEL 022 732 03 12
kupfer-geometre.ch
akupfer@worldcom.ch

Dossier : 2794
Date : 03.02.2023 / SP

N

Commune : Satigny
Section : –
Plan No : 72
Parcelle(s) : 7177
Echelle : 1:500

Provisoire à l'examen

PASSAGE : Passage public

Attention document PDF, déformation de l'échelle possible

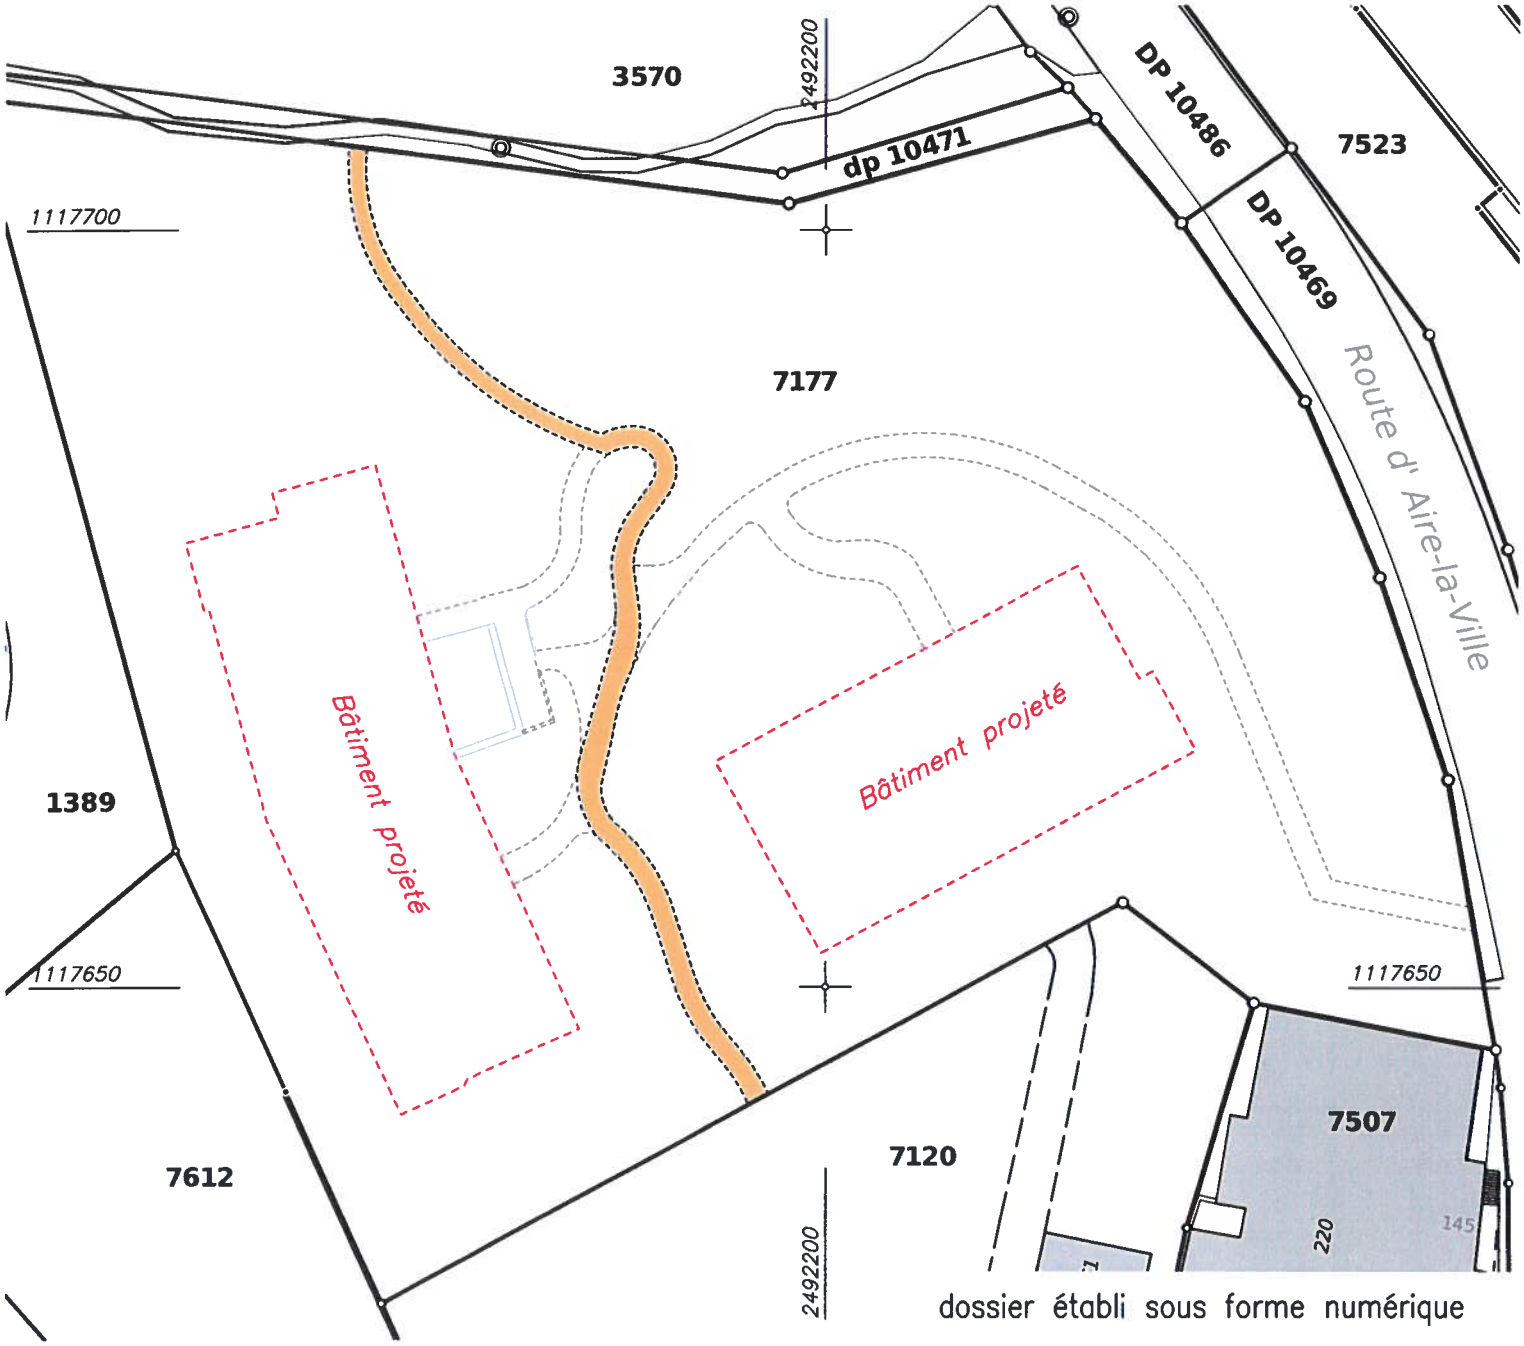

dossier établi sous forme numérique

P:\2750_2799\2794\Servitude\2794-V1-public_20230202

Plan de servitude

KÜPFER GÉOMÈTRES SA
INGÉNIEUR GÉOMÈTRE OFFICIEL EPF/AGG

RUE EUGÈNE-MARZIANO 41
CH 1227 LES ACACIAS
TEL 022 732 09 12
kupfer-geometre.ch
akupfer@worldcom.ch

Dossier : 2794
Date : 15.12.2023 / GDC

N

Commune	:	Satigny
Section	:	–
Plan No	:	72
Parcelle(s)	:	7177
Echelle	:	1:500

Provisoire à l'examen

USAGE : Usage de places de stationnement visiteurs V1 à V4 au sous-sol

Attention document PDF, déformation de l'échelle possible

dossier établi sous forme numérique

P:\2750_2799\2794\Servitude\2794-V1-public_20230202